

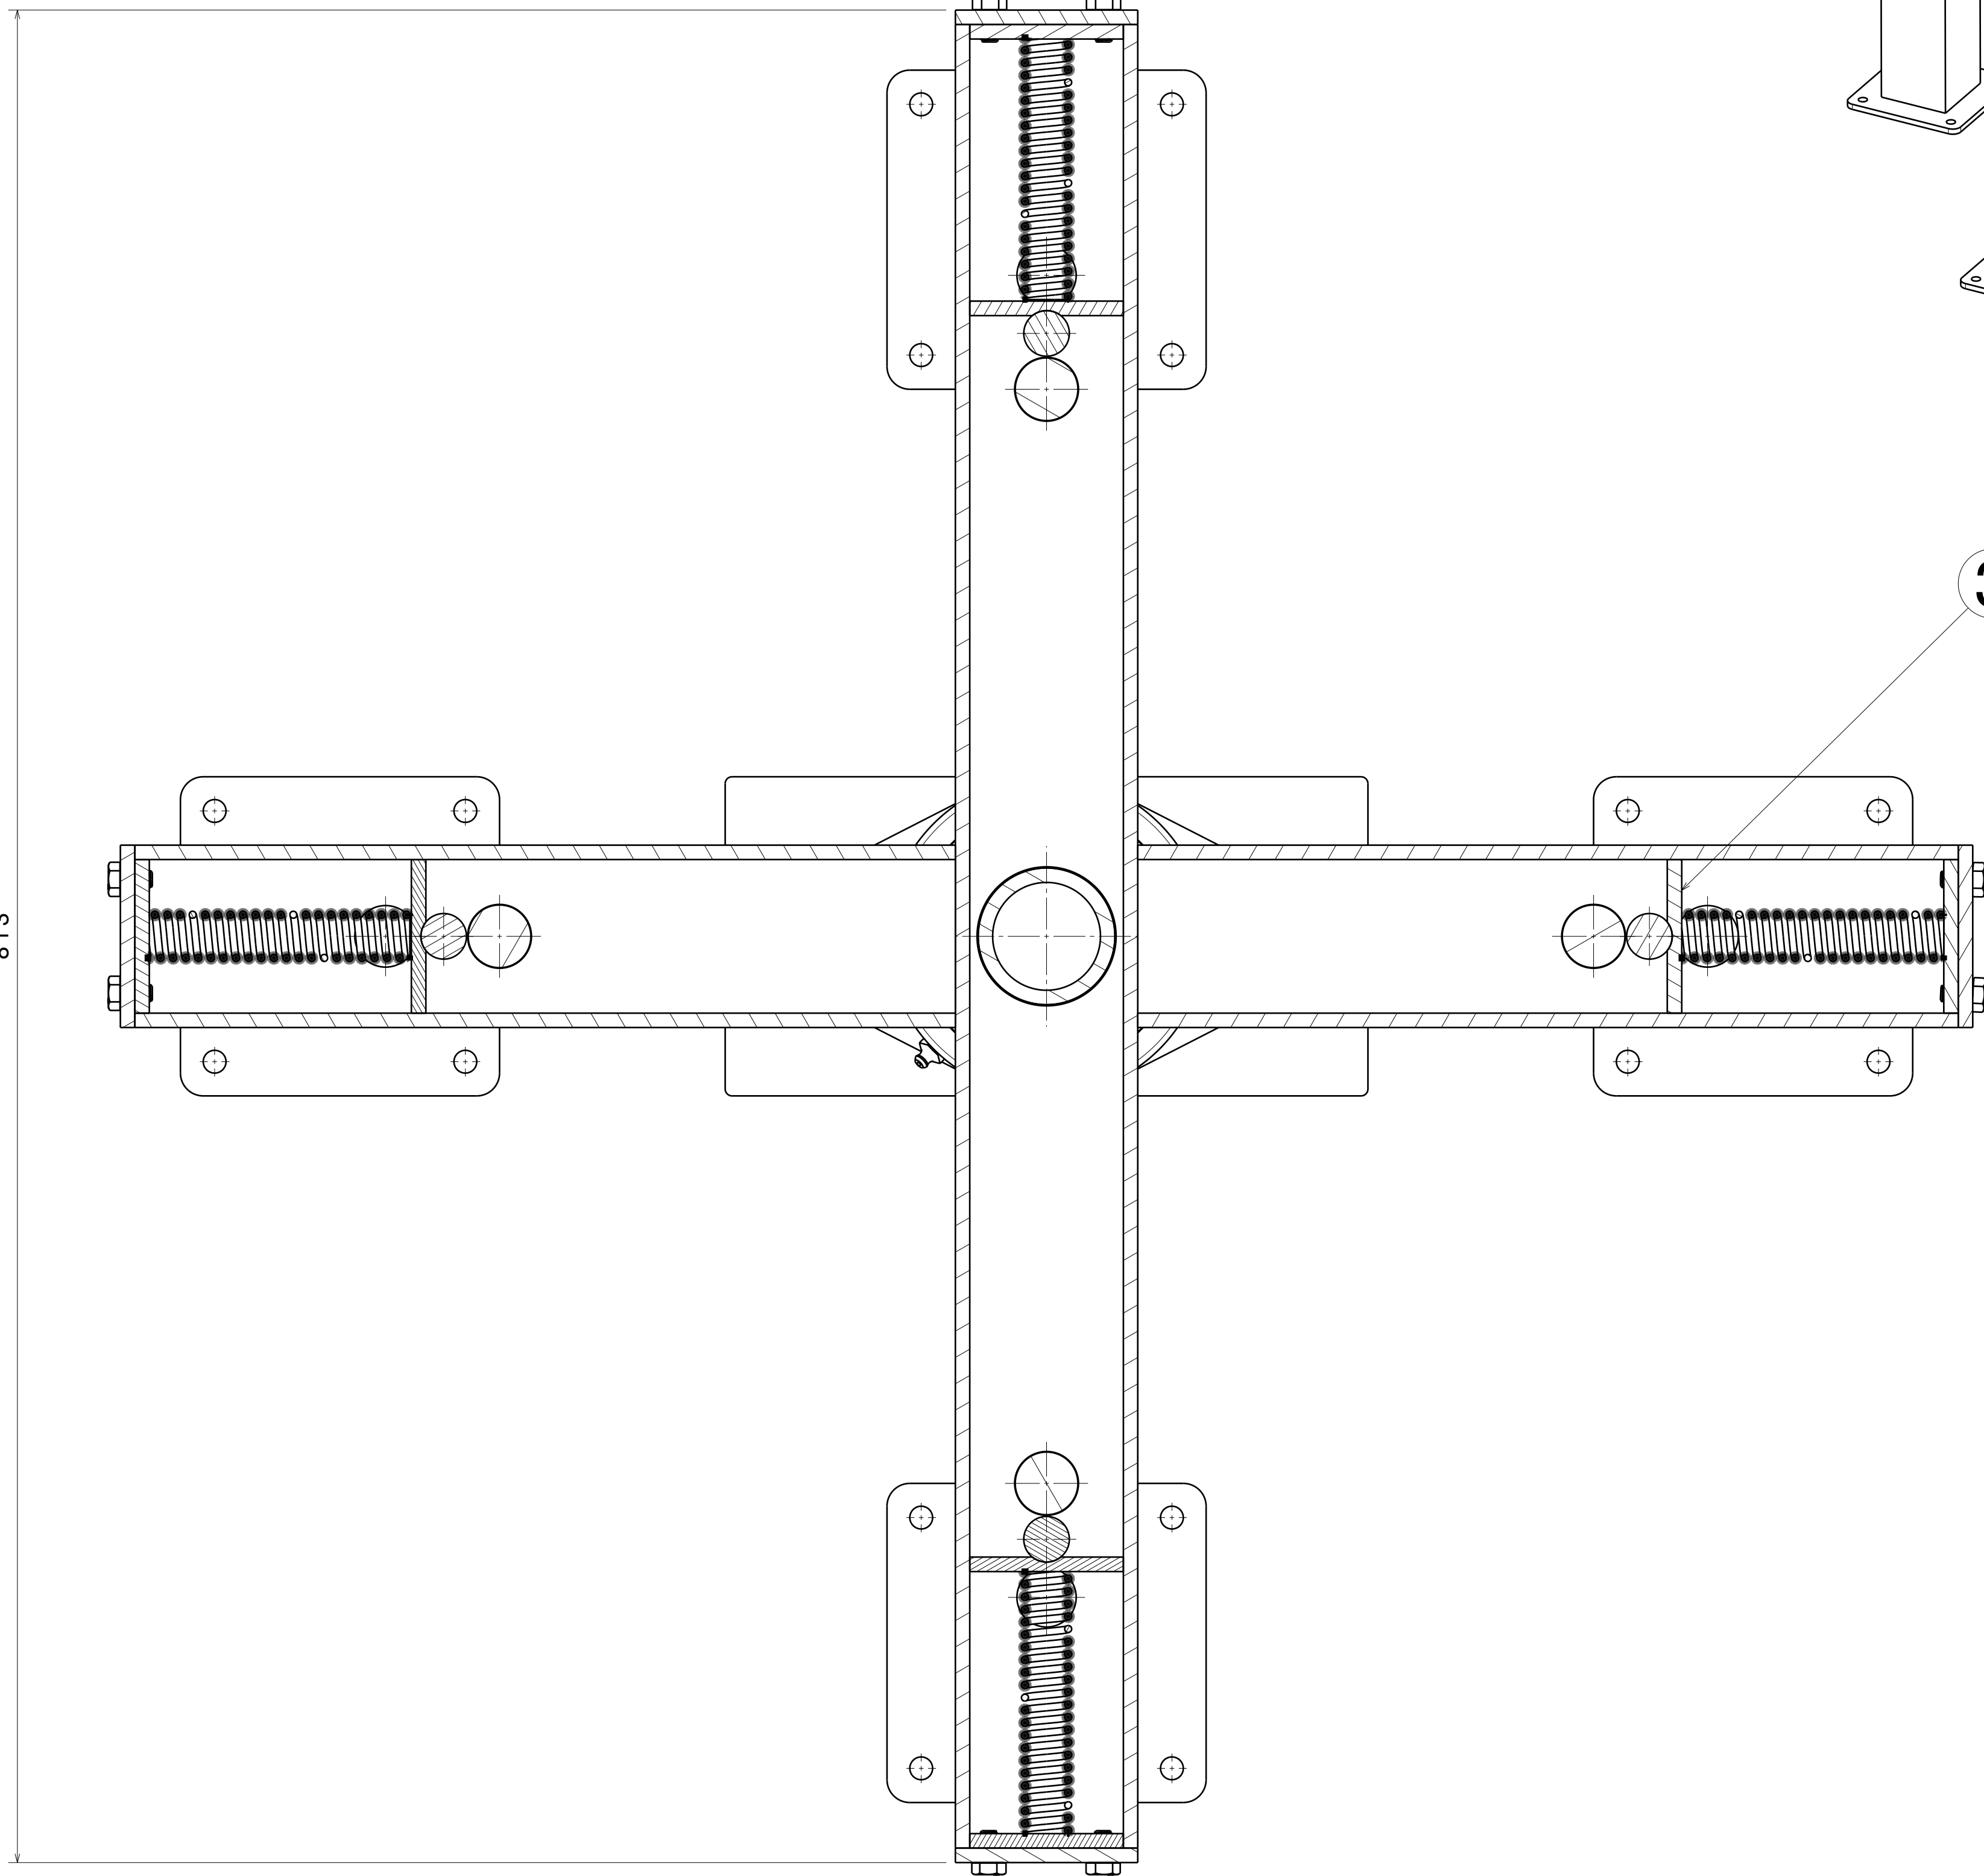
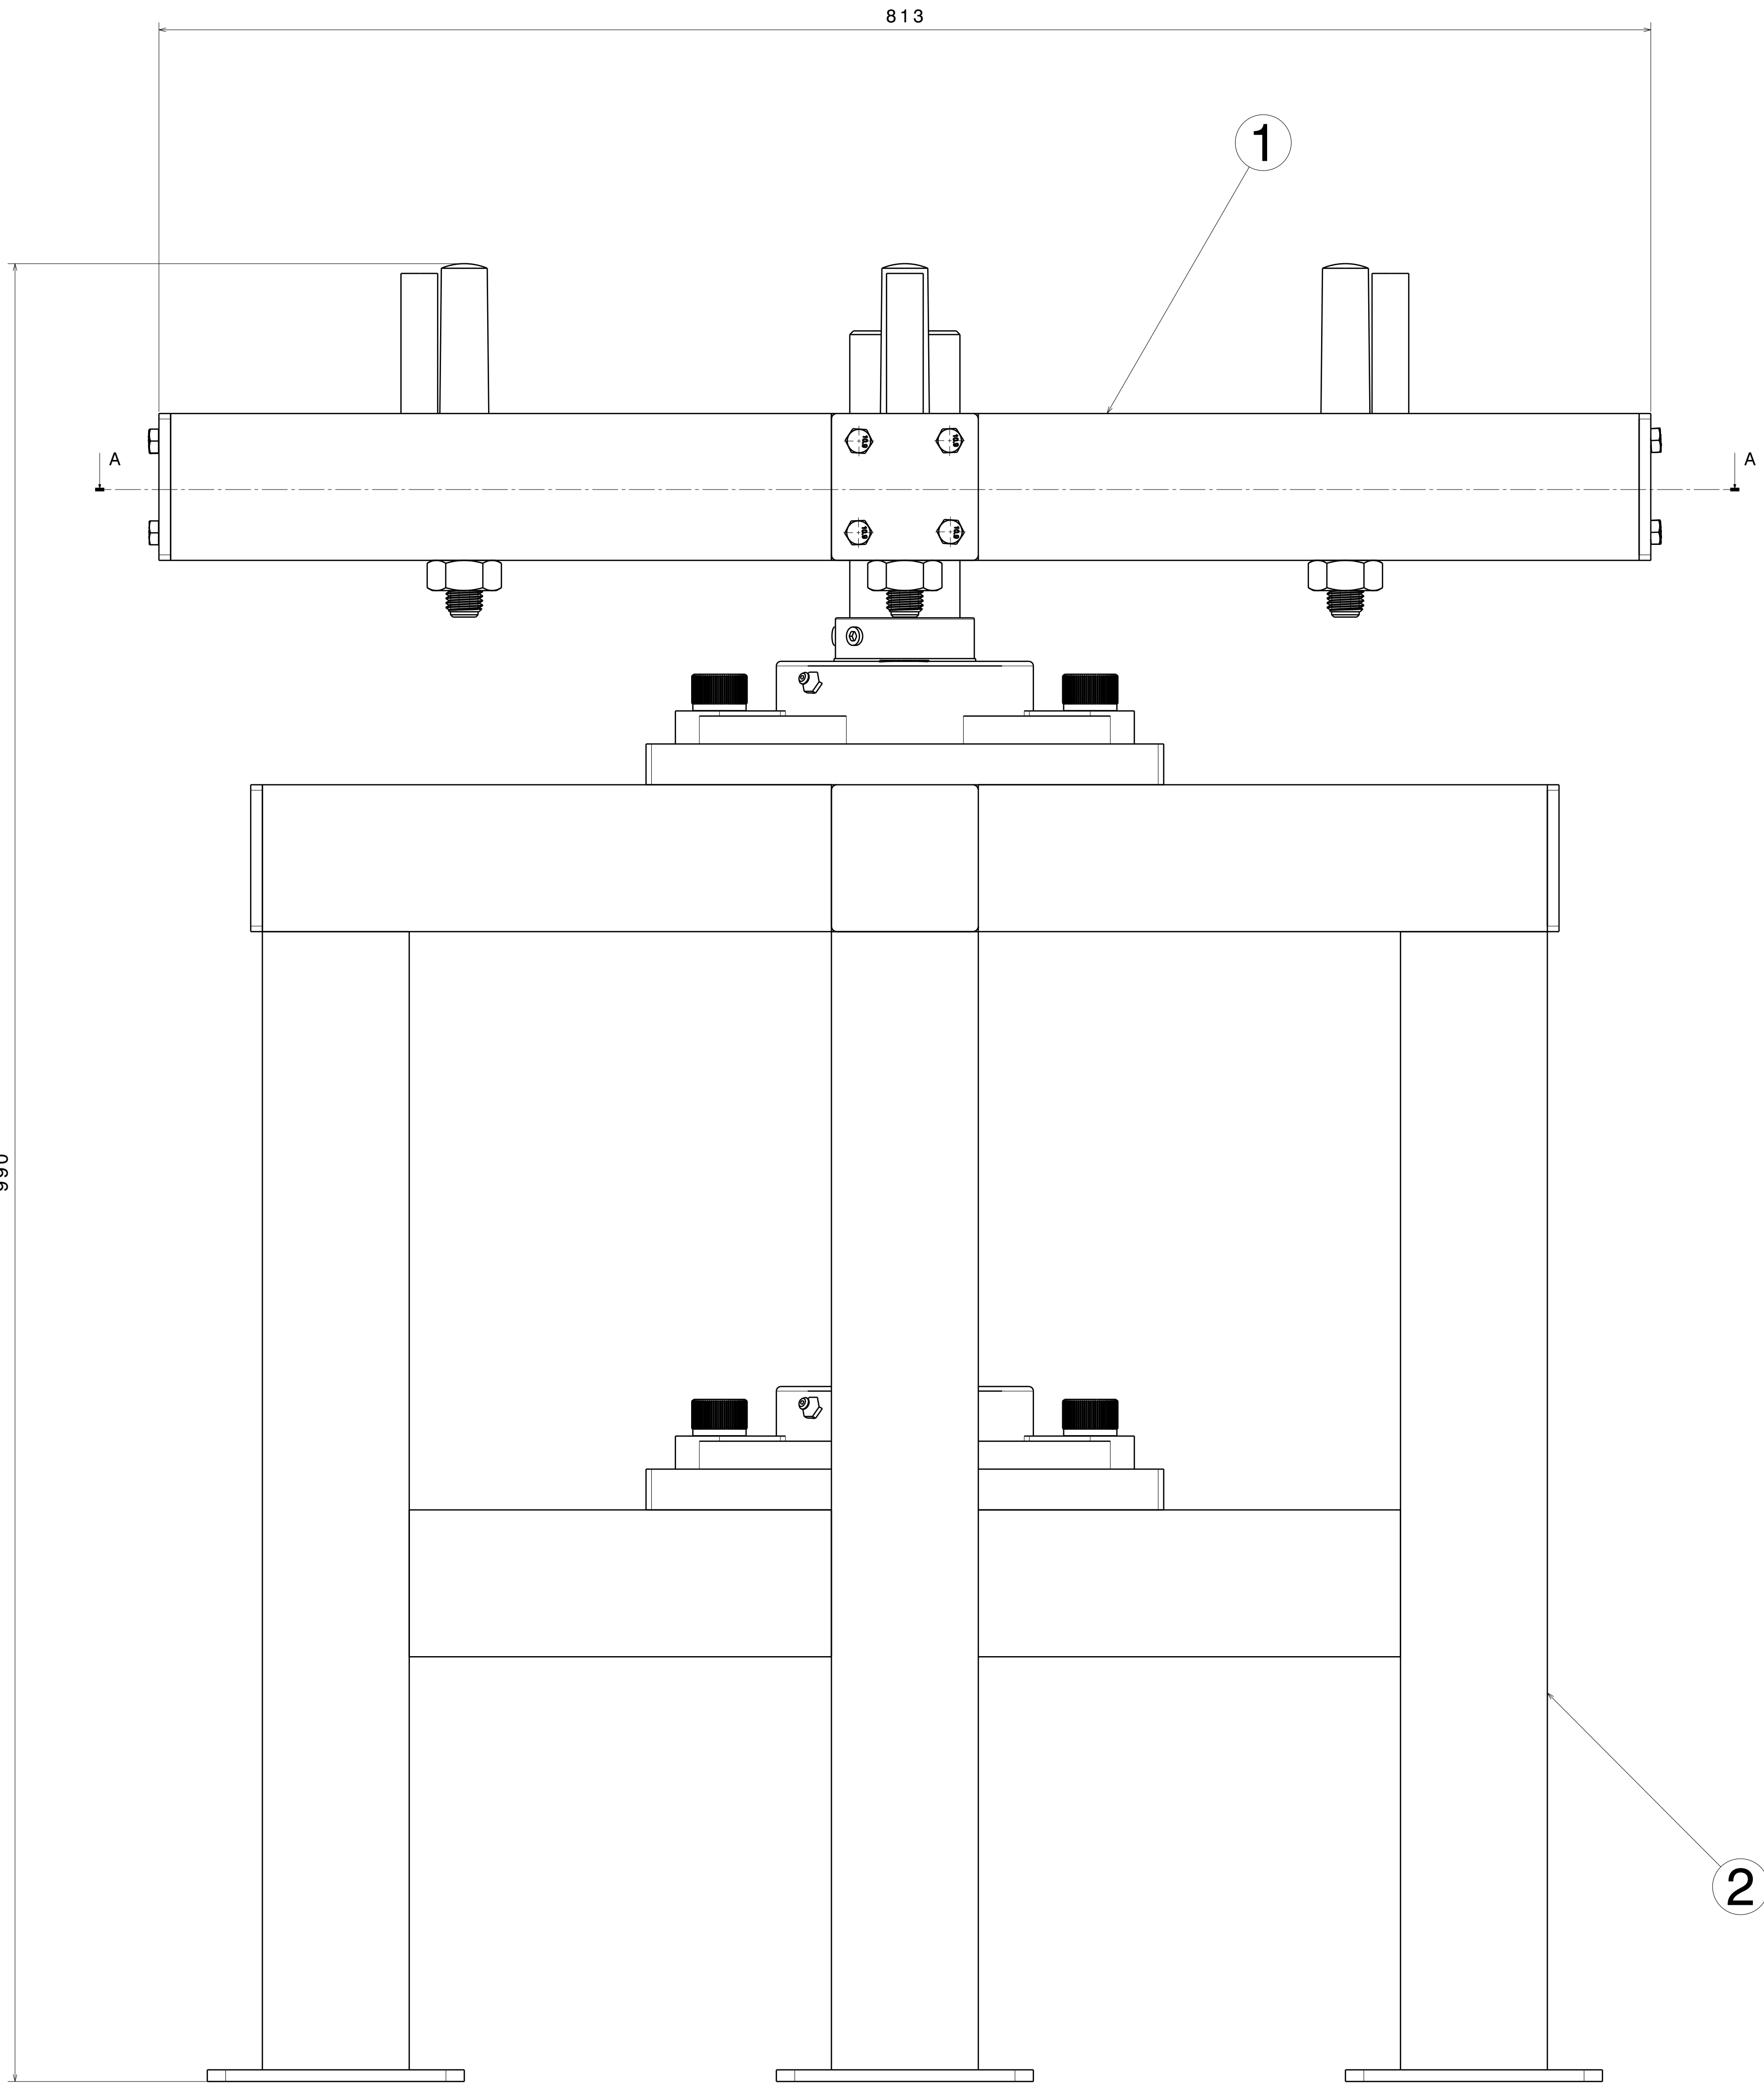


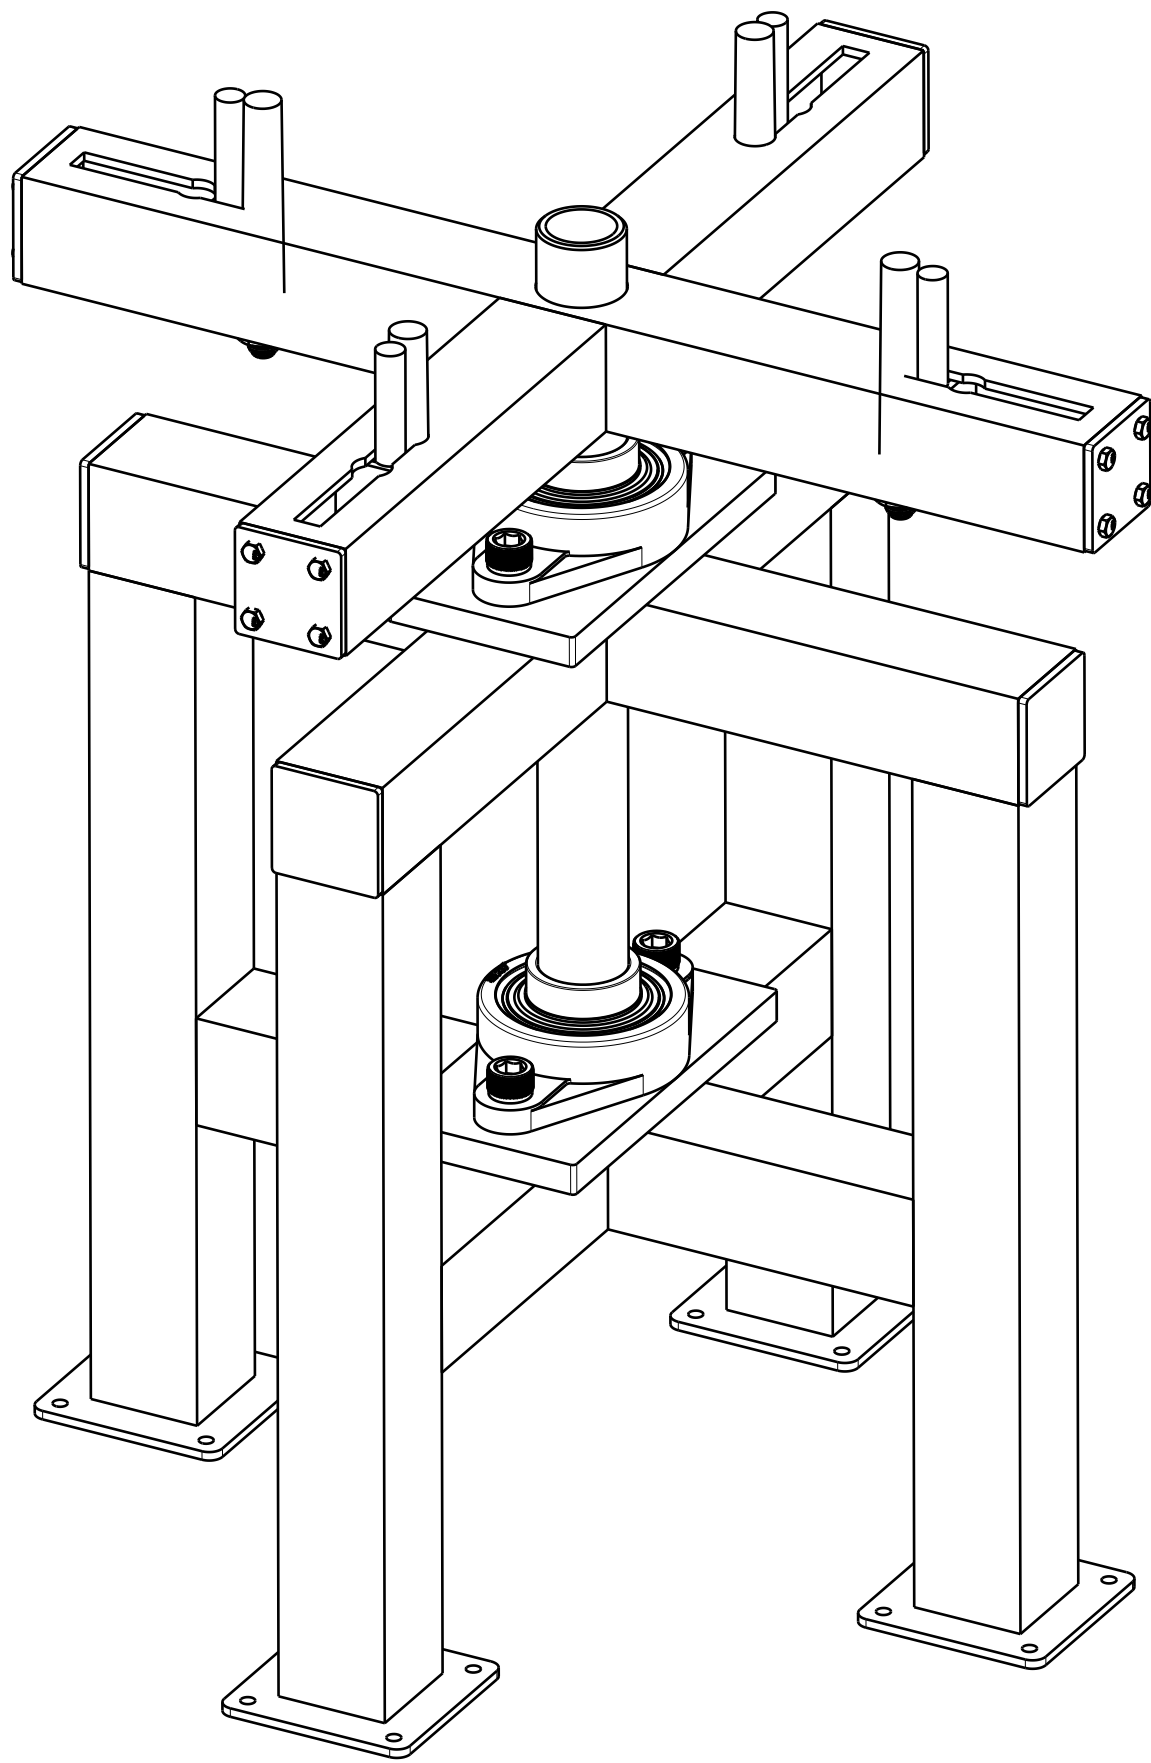

CORTE A-A

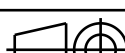

VISTA ISOMETRICA
ESCALA 1:5

3	1	001-002-003-000	Estructura metálica		
2	4	001-002-002-000	Conjunto apriete		
1	1	001-002-001-000	Soporte principal		
Item		Cantidad	Modelo	Descripción	
Tolerancias Generales		Proyectó	Grupo	Ing. Mecánica	
		Dibujó	Grupo		
		Revisó	Grupo		
		Aprobó	Grupo		
		Escala			
		1:2			
					
CARRETE					
			Universidad Nacional de Córdoba		
			001-002-000-000		
					
				Pag. 1	