
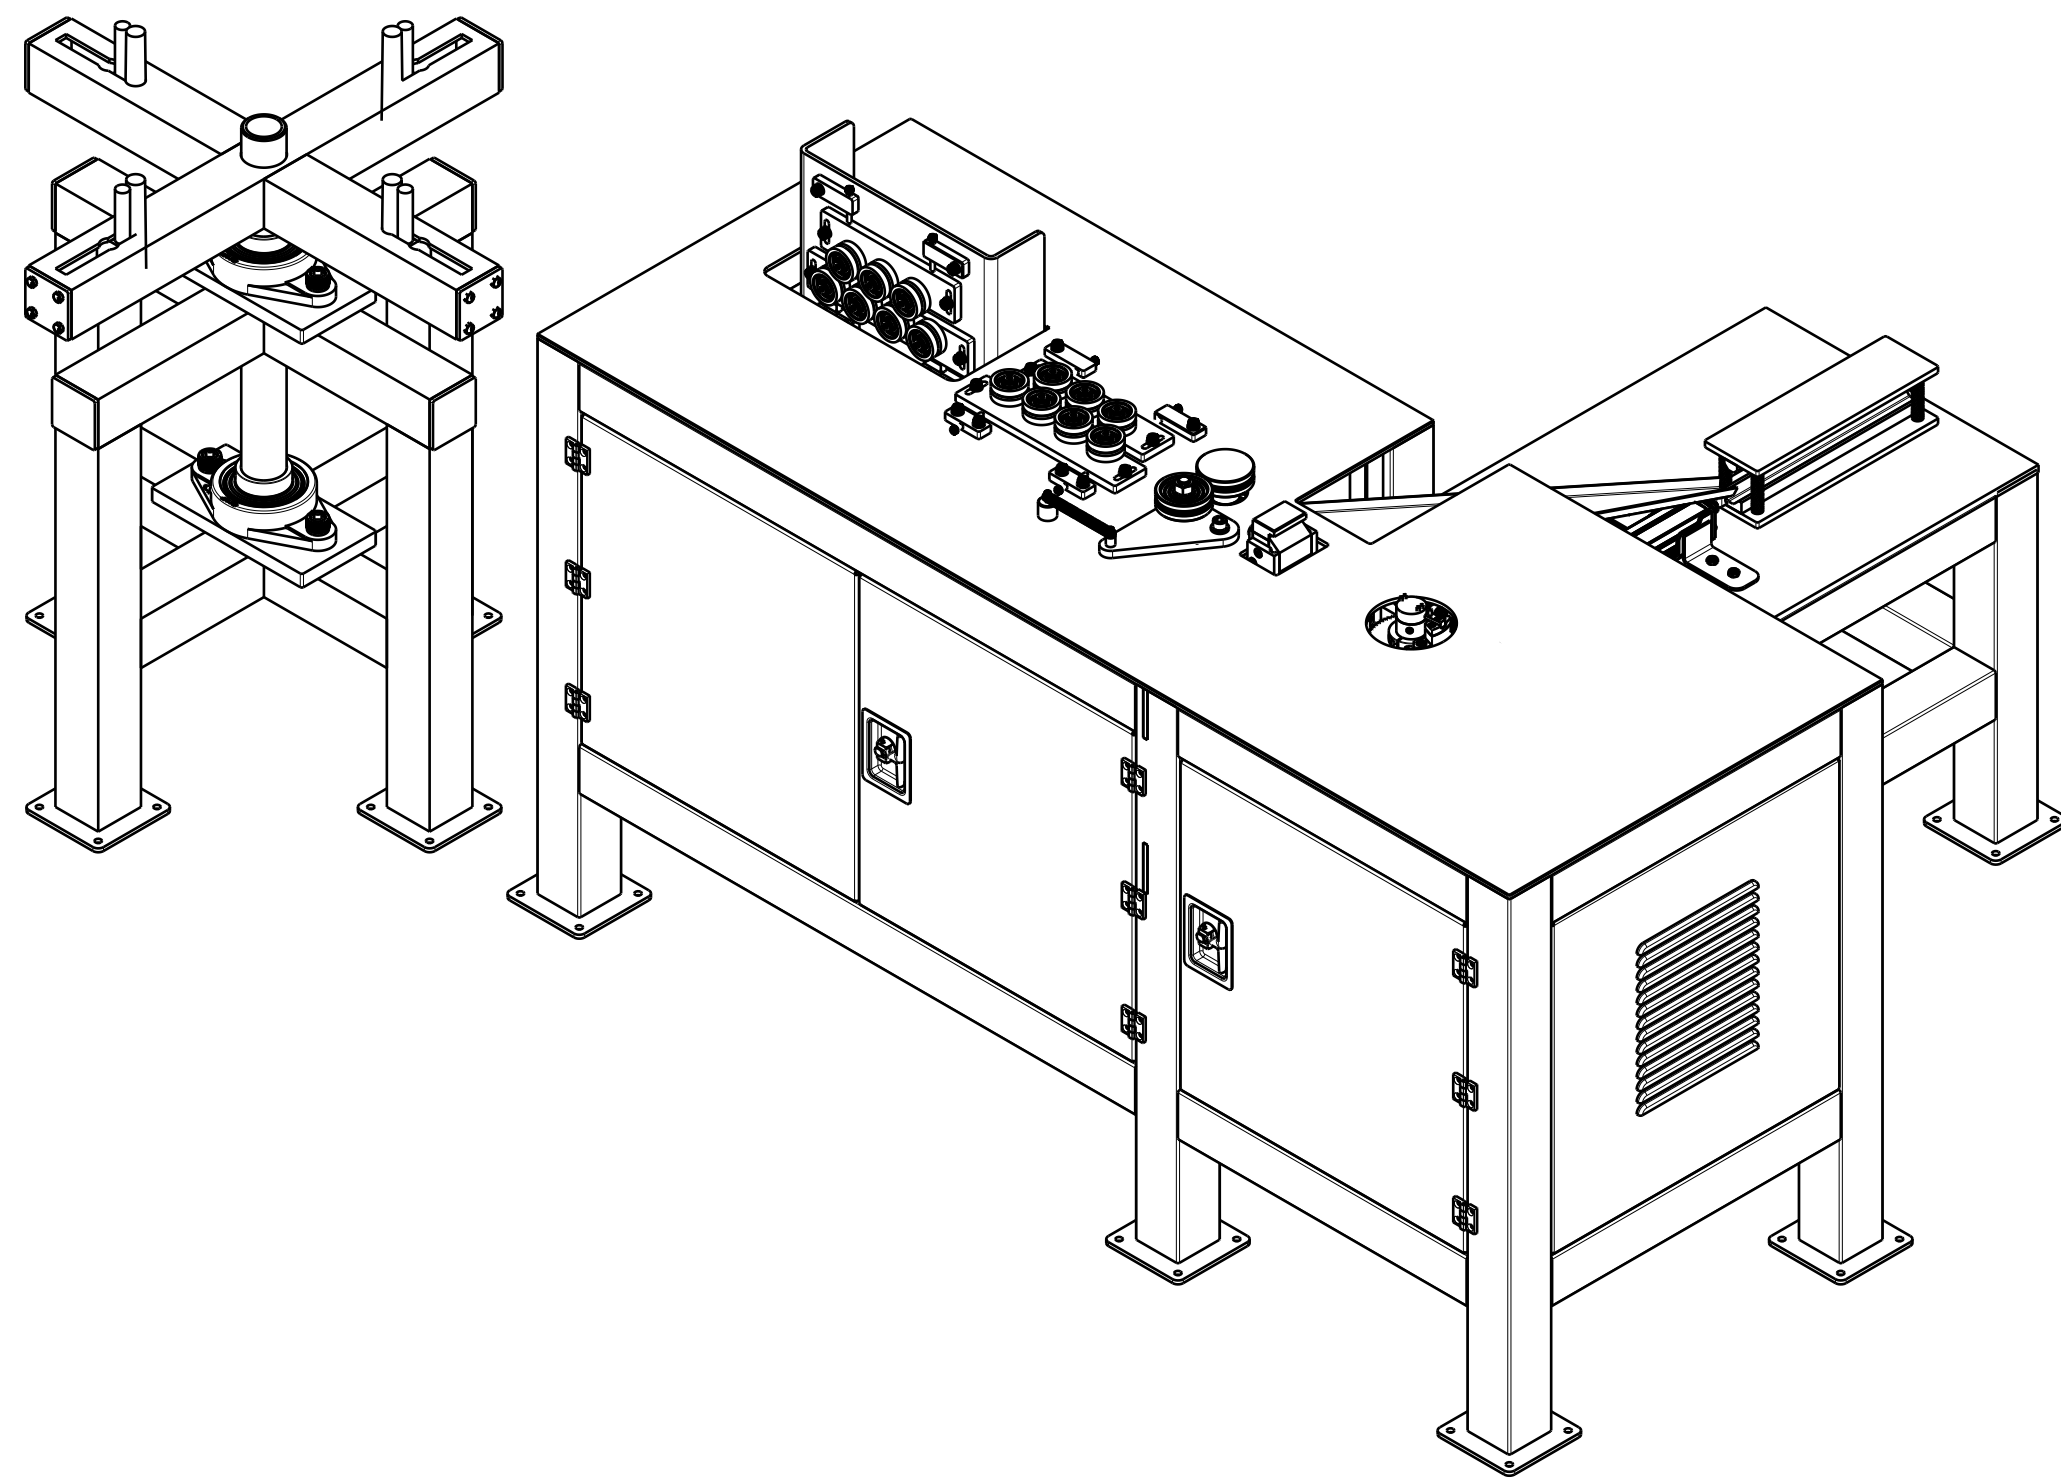
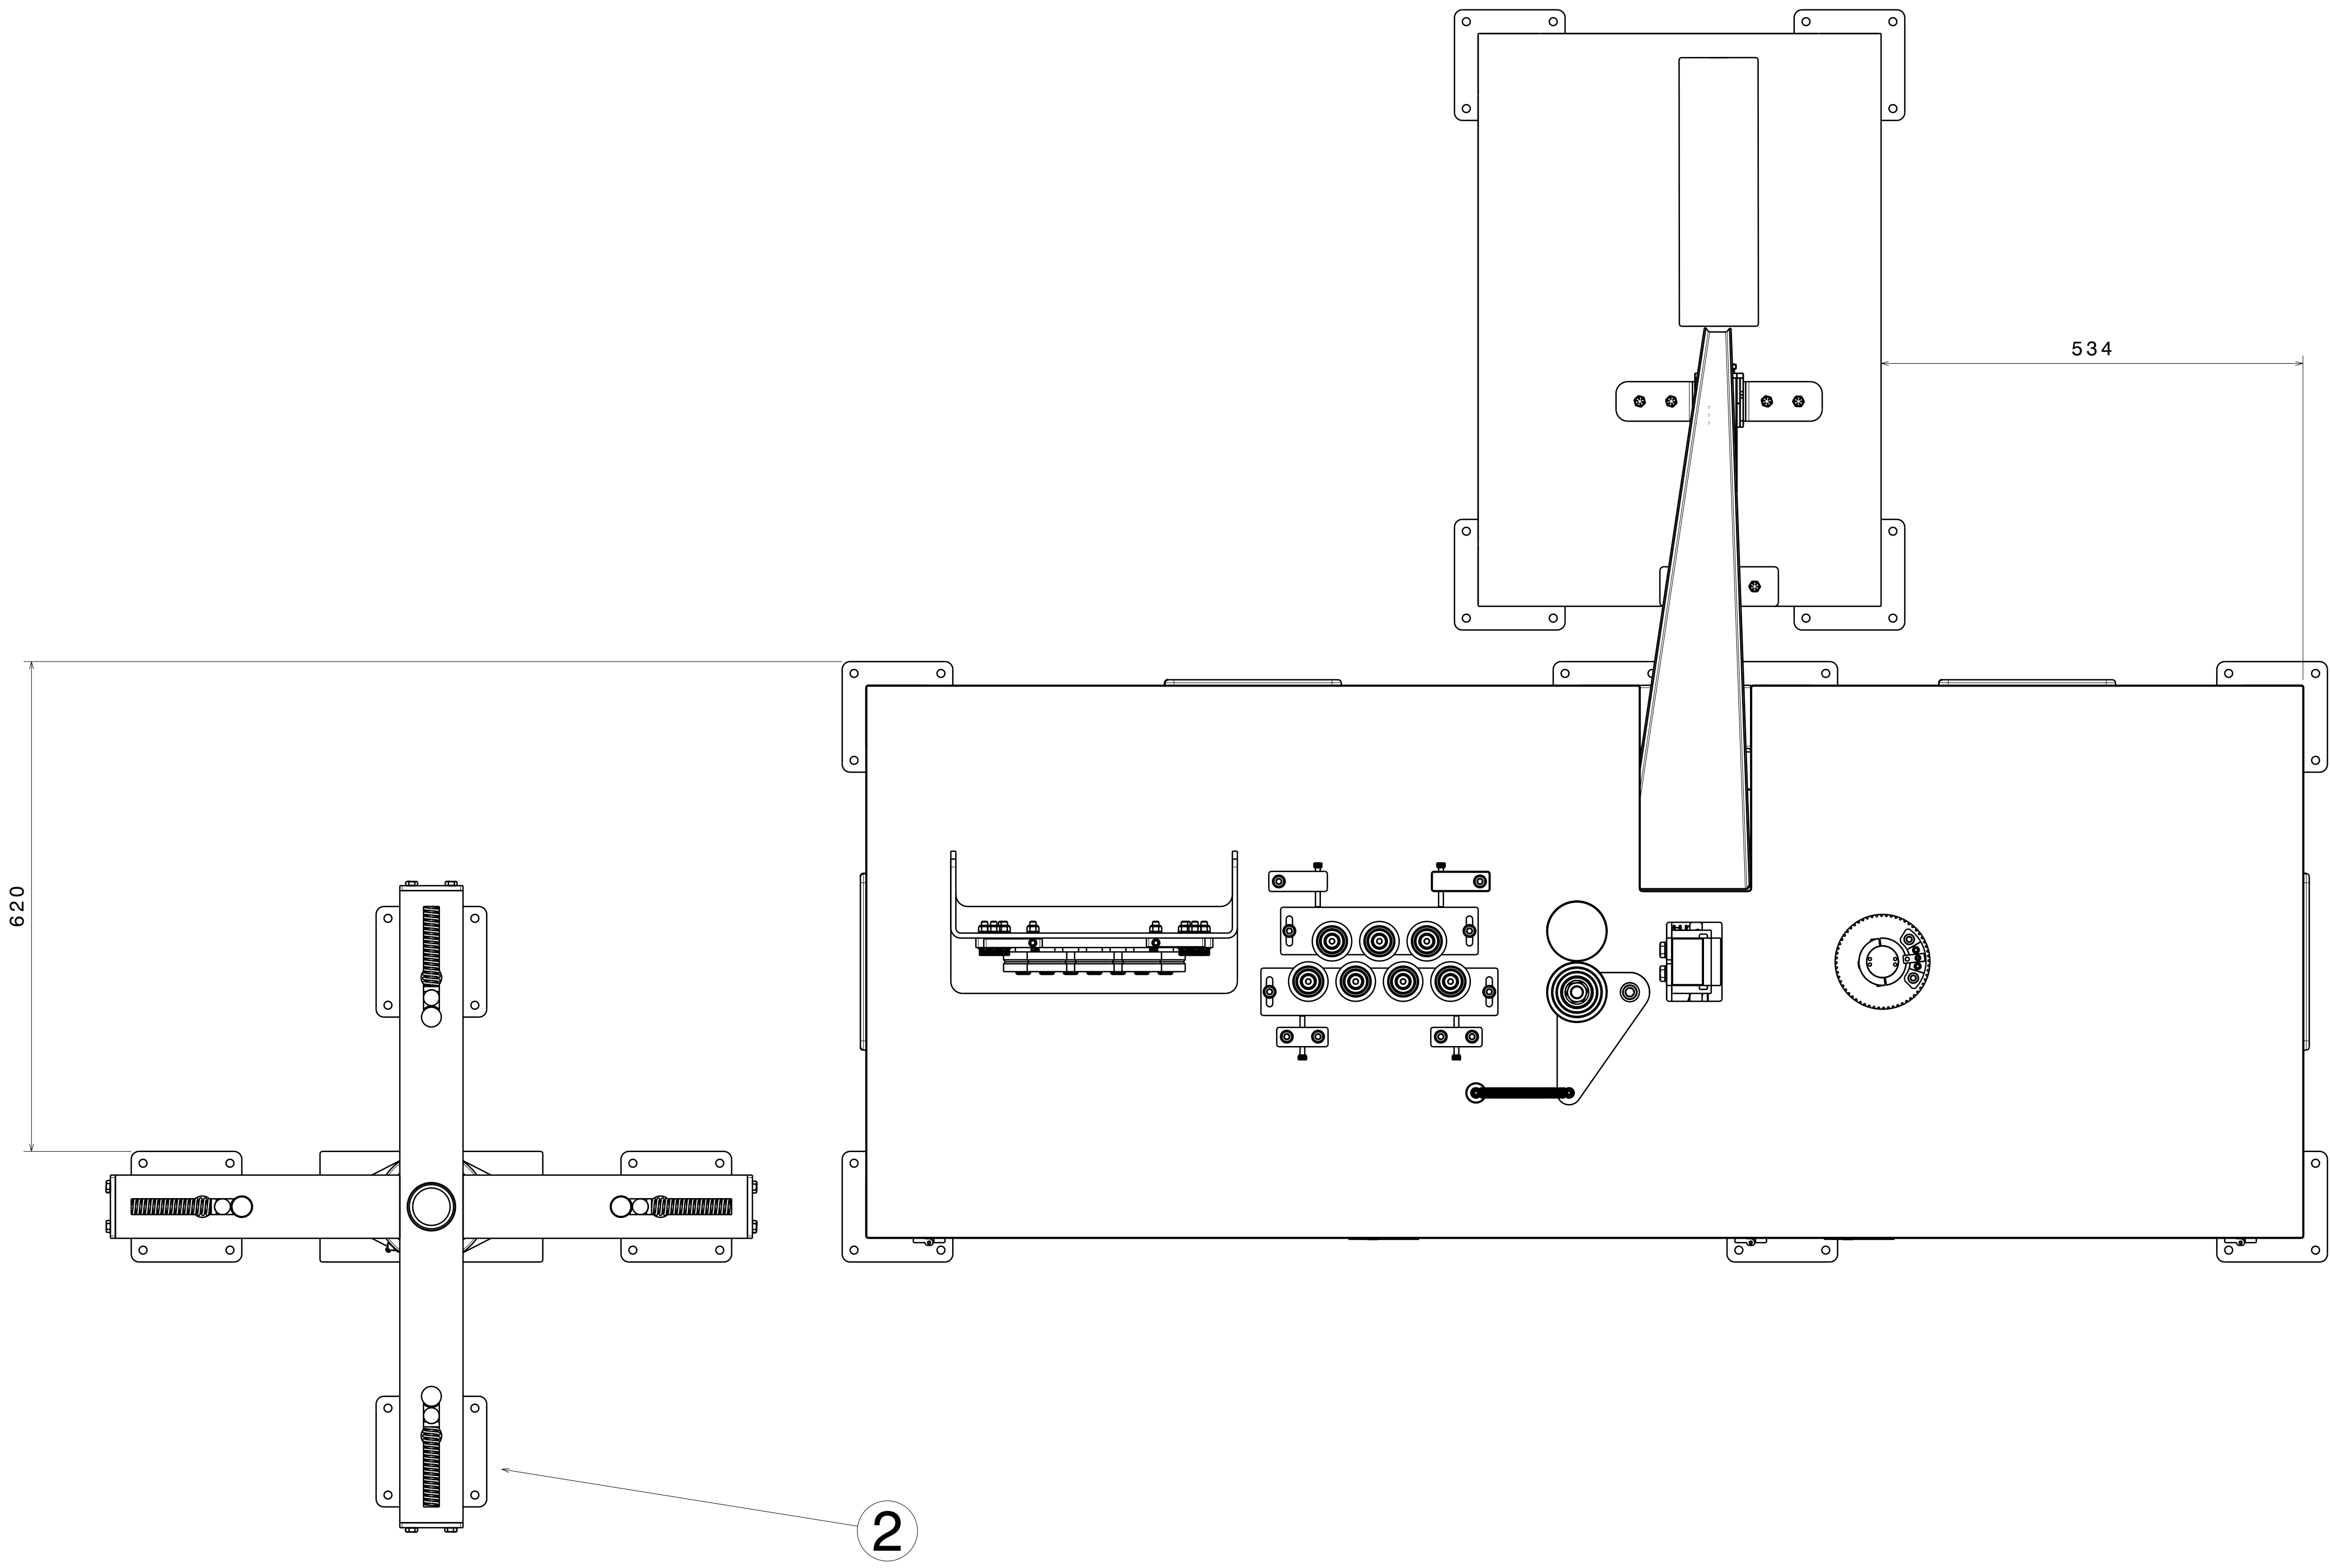
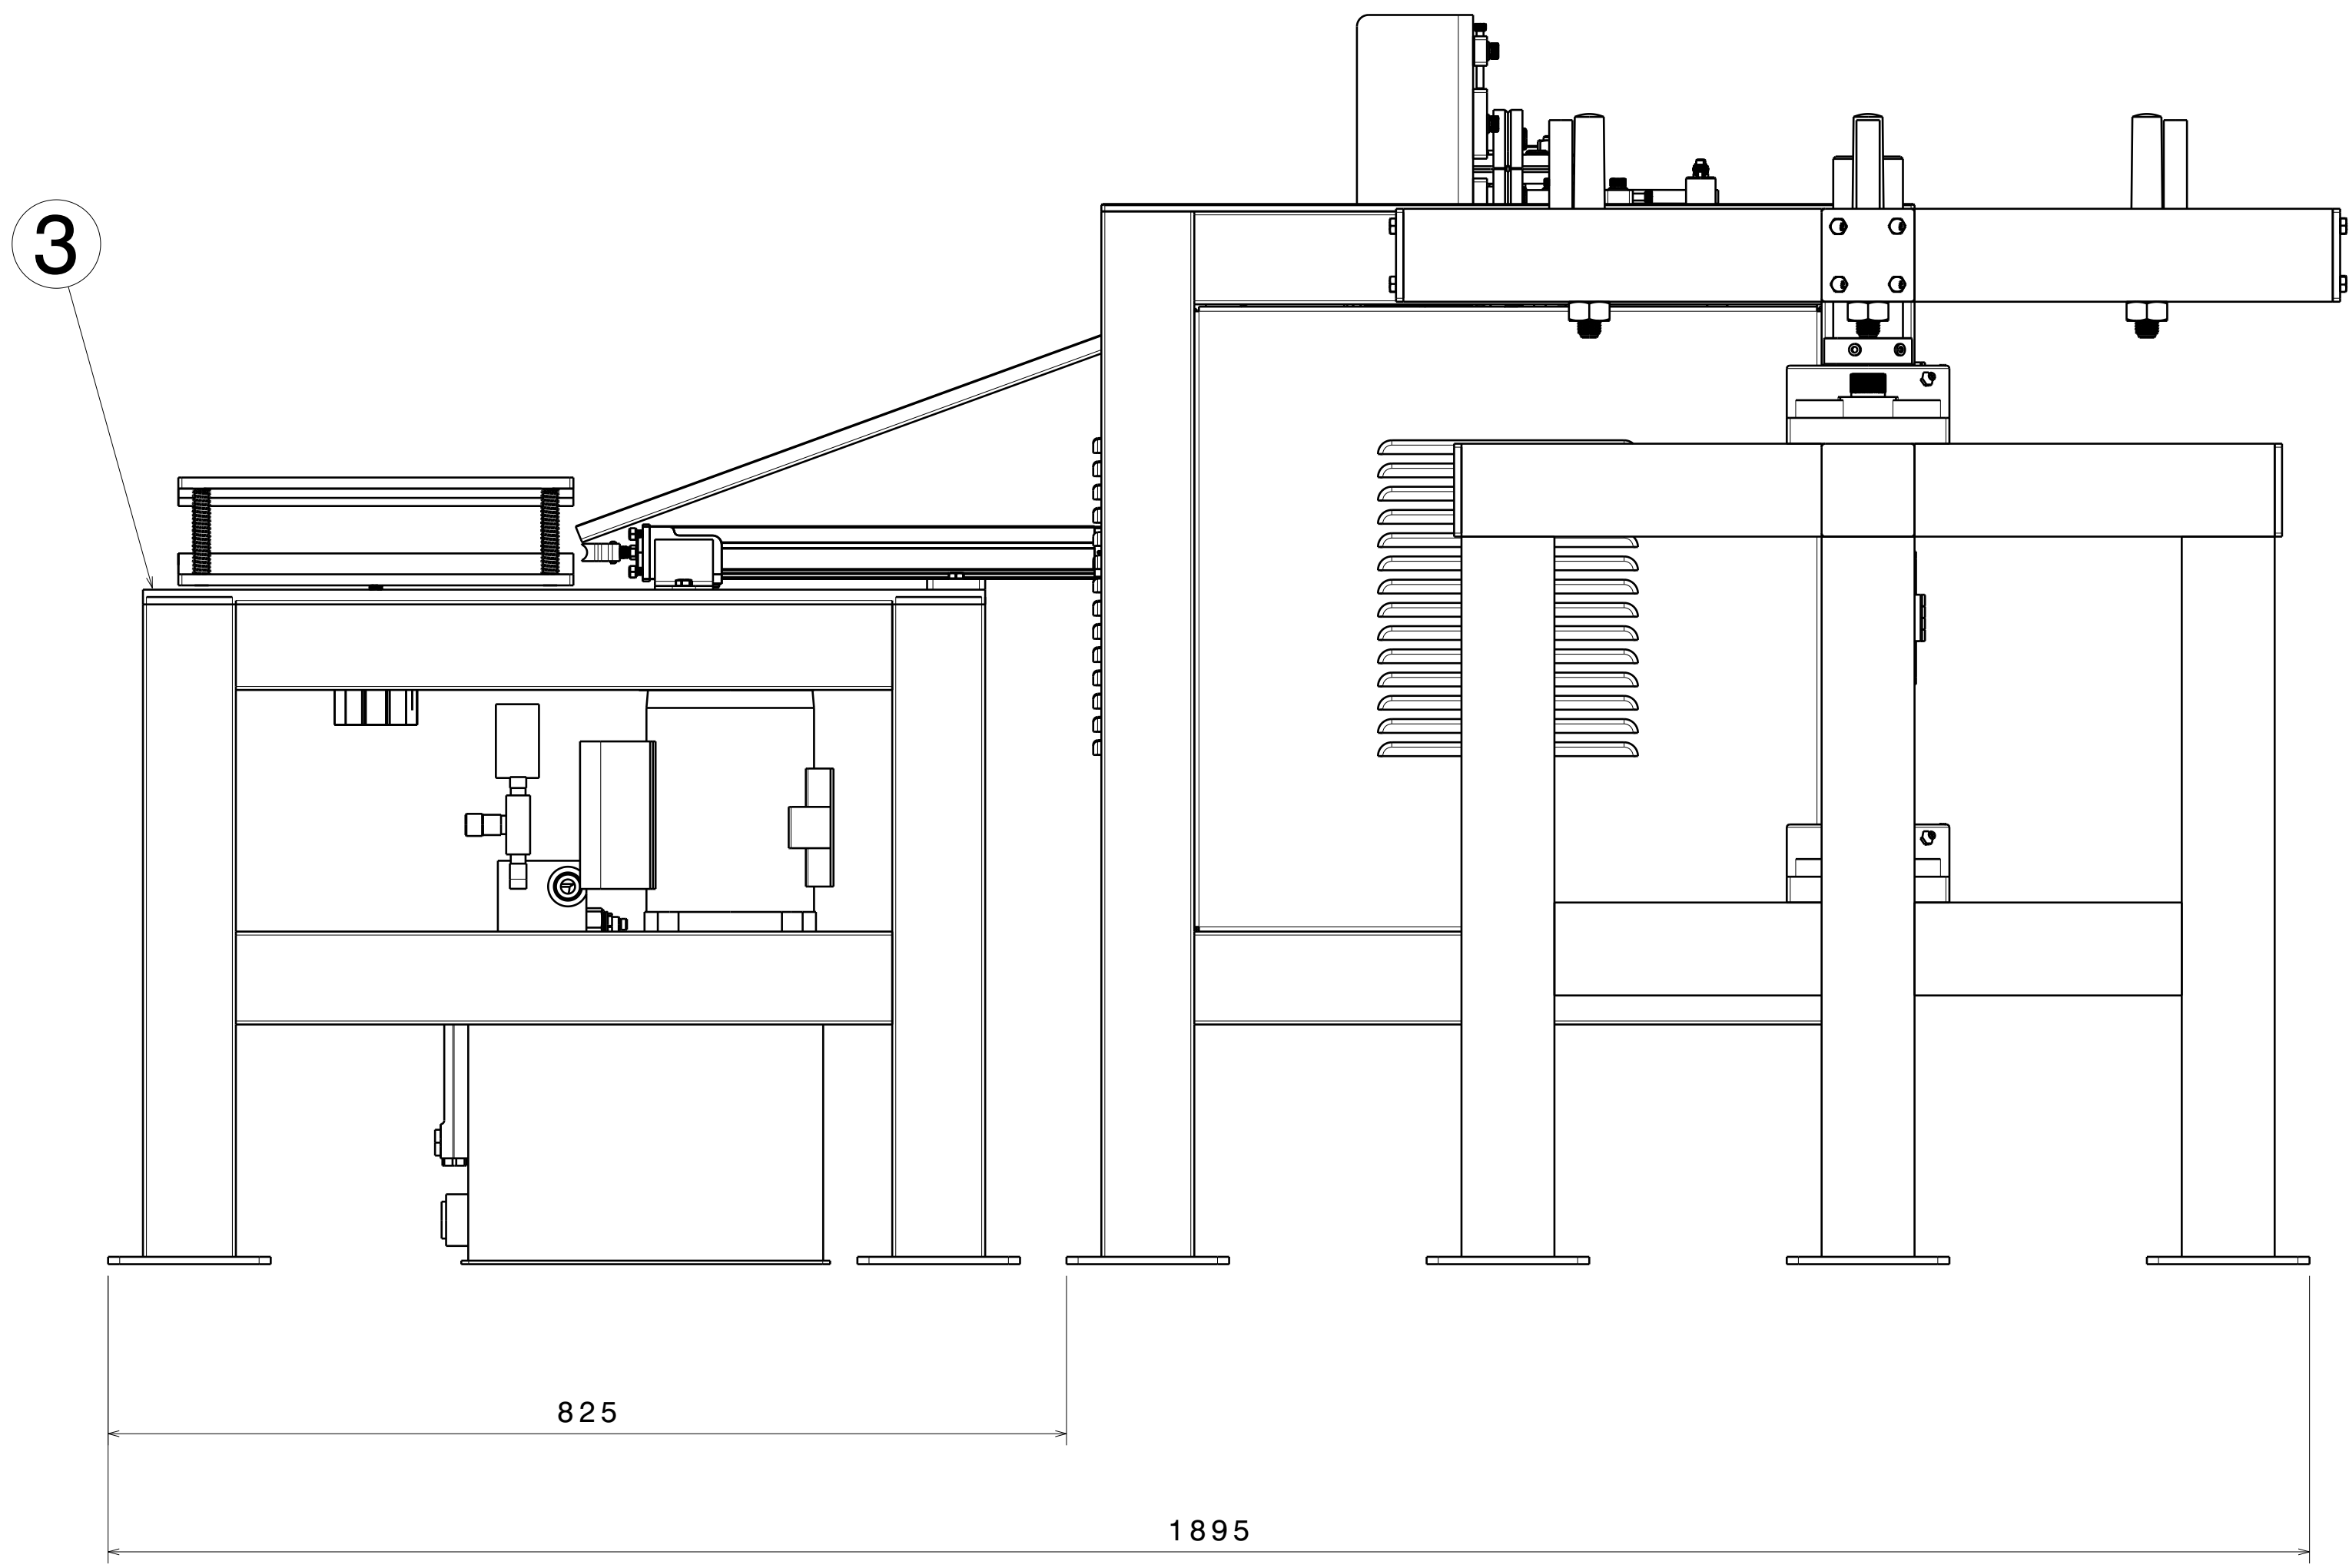


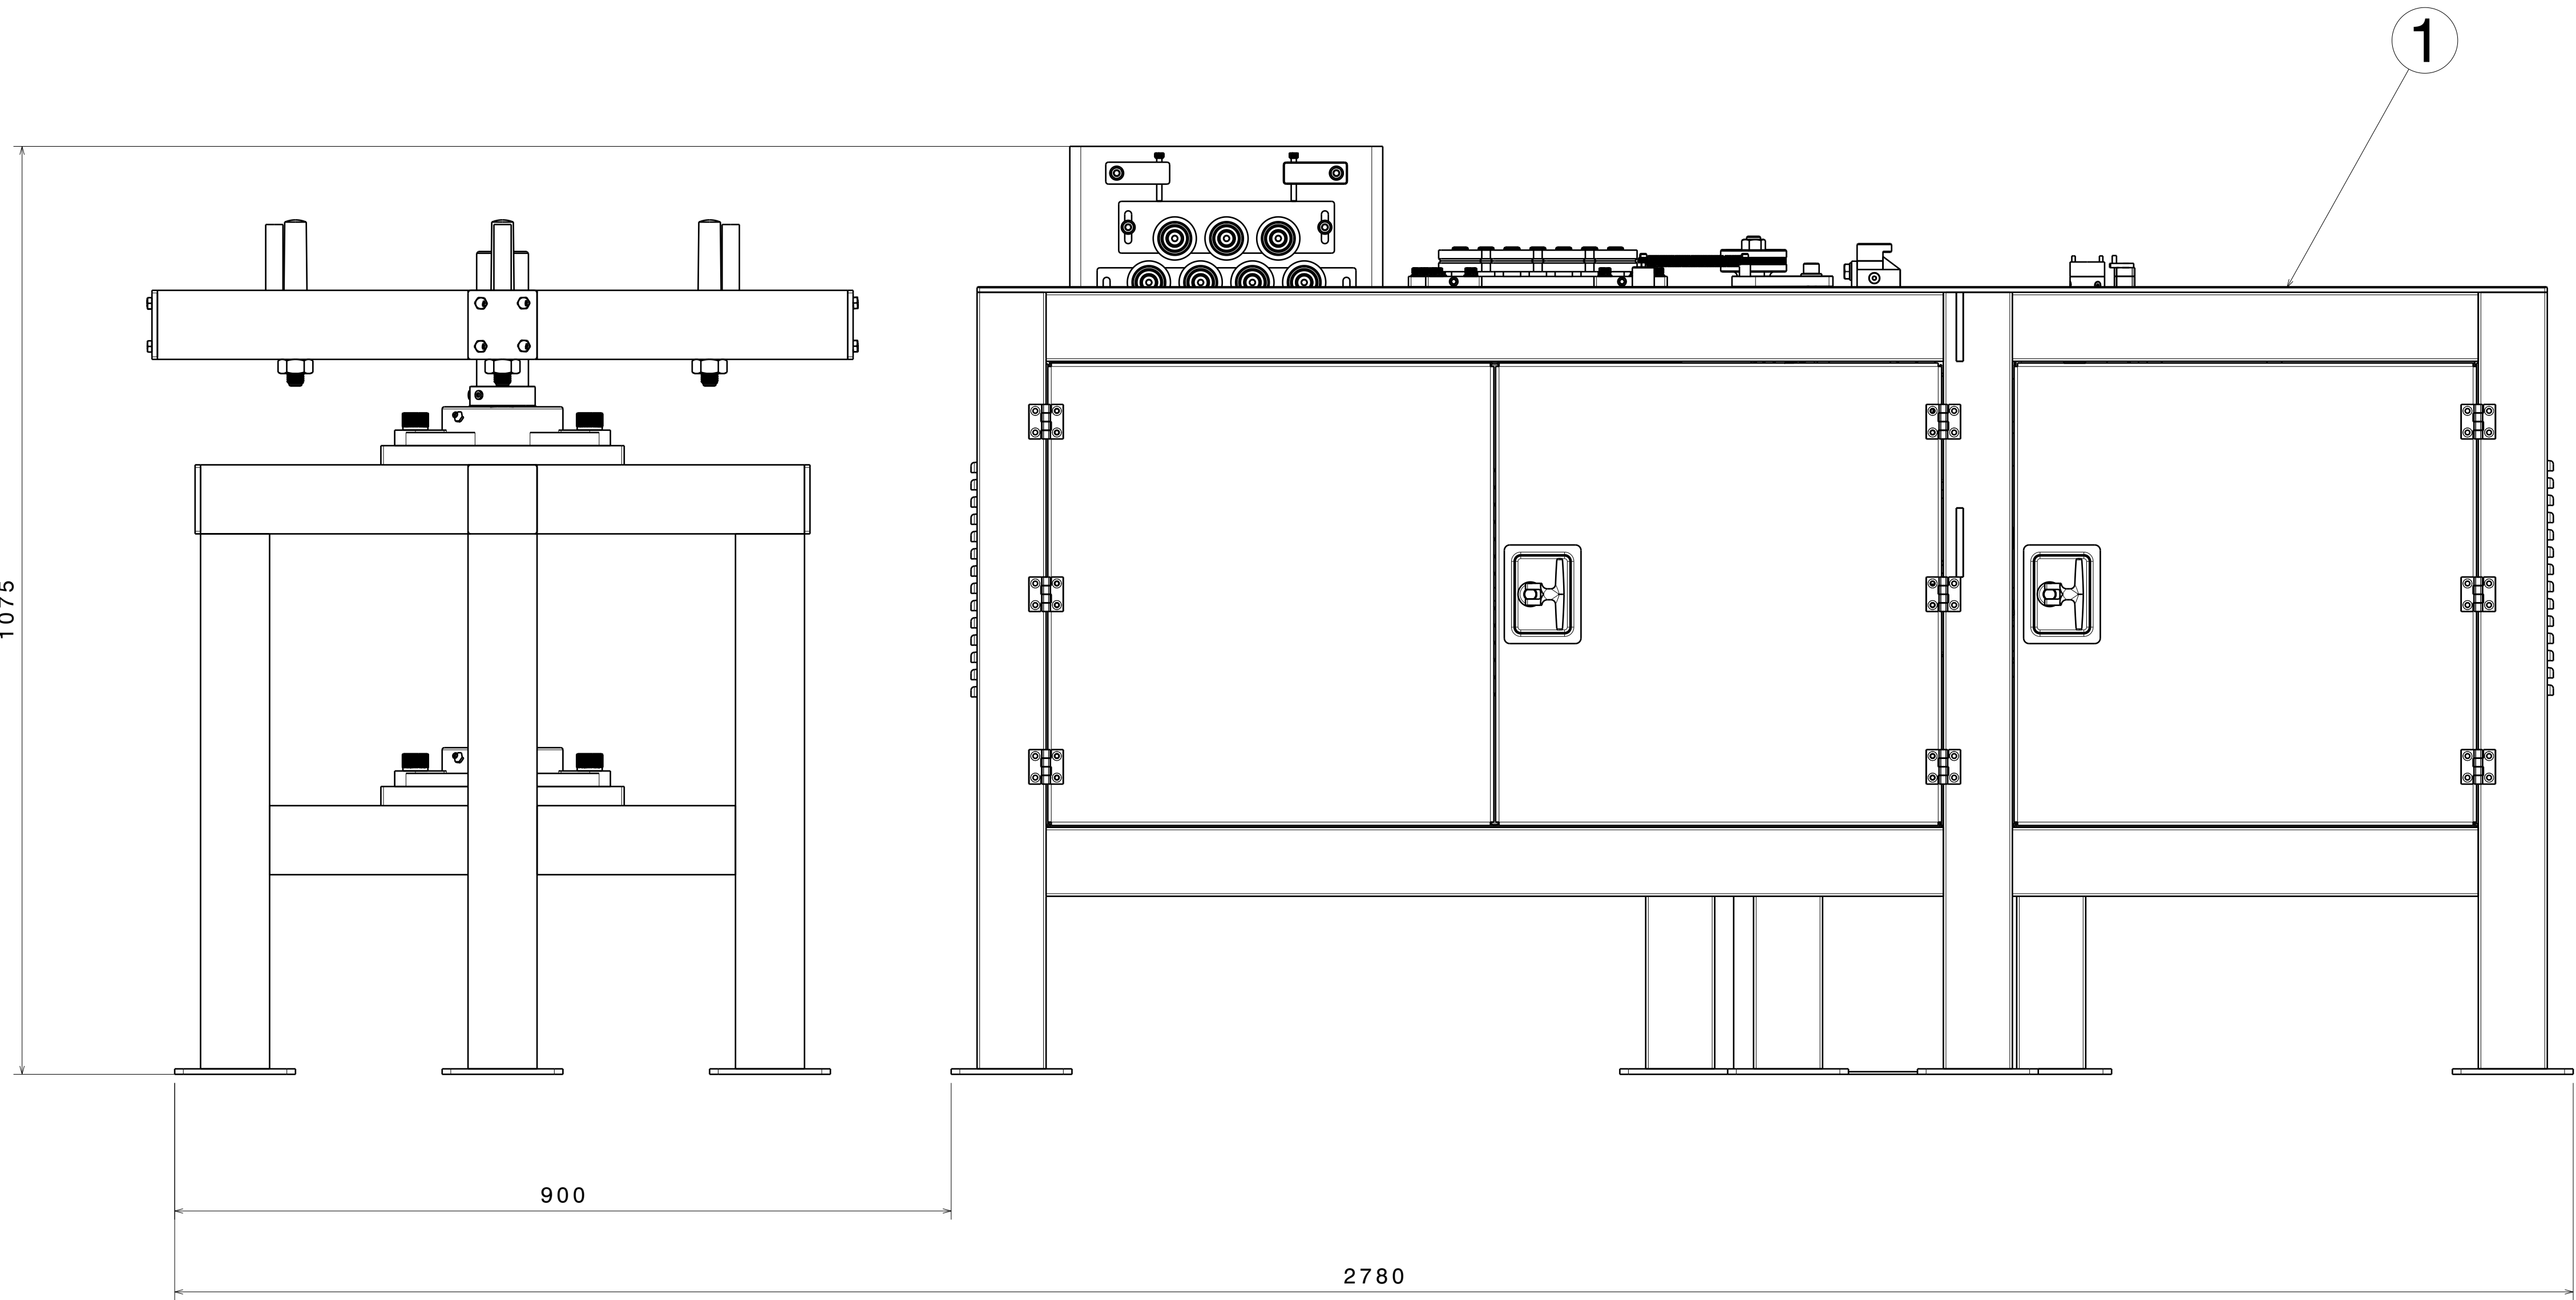

Vista isométrica  
Escala: 1:10

|                       |   |                  |                                 |               |                                                                                       |
|-----------------------|---|------------------|---------------------------------|---------------|---------------------------------------------------------------------------------------|
| 1                     | 1 | 001-003-000-000  | Prensa                          |               |                                                                                       |
| 1                     | 1 | 001-002-000-000  | Carrete                         |               |                                                                                       |
| 1                     | 1 | 001-001-000-000  | Dobladora de alambre            |               |                                                                                       |
| Item                  |   | Cantidad         | Modelo                          | Descripción   |                                                                                       |
| Tolerancias Generales |   | Proyecto         | Grupo                           | Ing. Mecánica | Fecha: 17/06/25                                                                       |
|                       |   | Dibujó           | Grupo                           |               | Medidas en: mm                                                                        |
|                       |   | Revisó           | Grupo                           |               |                                                                                       |
|                       |   | Aprobó           | Grupo                           |               |                                                                                       |
|                       |   | Escala           | UNIVERSIDAD NACIONAL DE CORDOBA |               |                                                                                       |
|                       |   | 1:5              |                                 |               |                                                                                       |
|                       |   | CONJUNTO GENERAL |                                 |               |  |
|                       |   |                  |                                 |               |                                                                                       |
|                       |   | Formato A0       | 001-000-000-000                 |               |                                                                                       |
|                       |   |                  | Pag. 2                          |               |                                                                                       |